


A-101 / SYNTHETIC PLAN

SYNTHETIC - NOT FOR CONSTRUCTION


No real site or design. Diagram coordinates are uncalibrated fixture units.

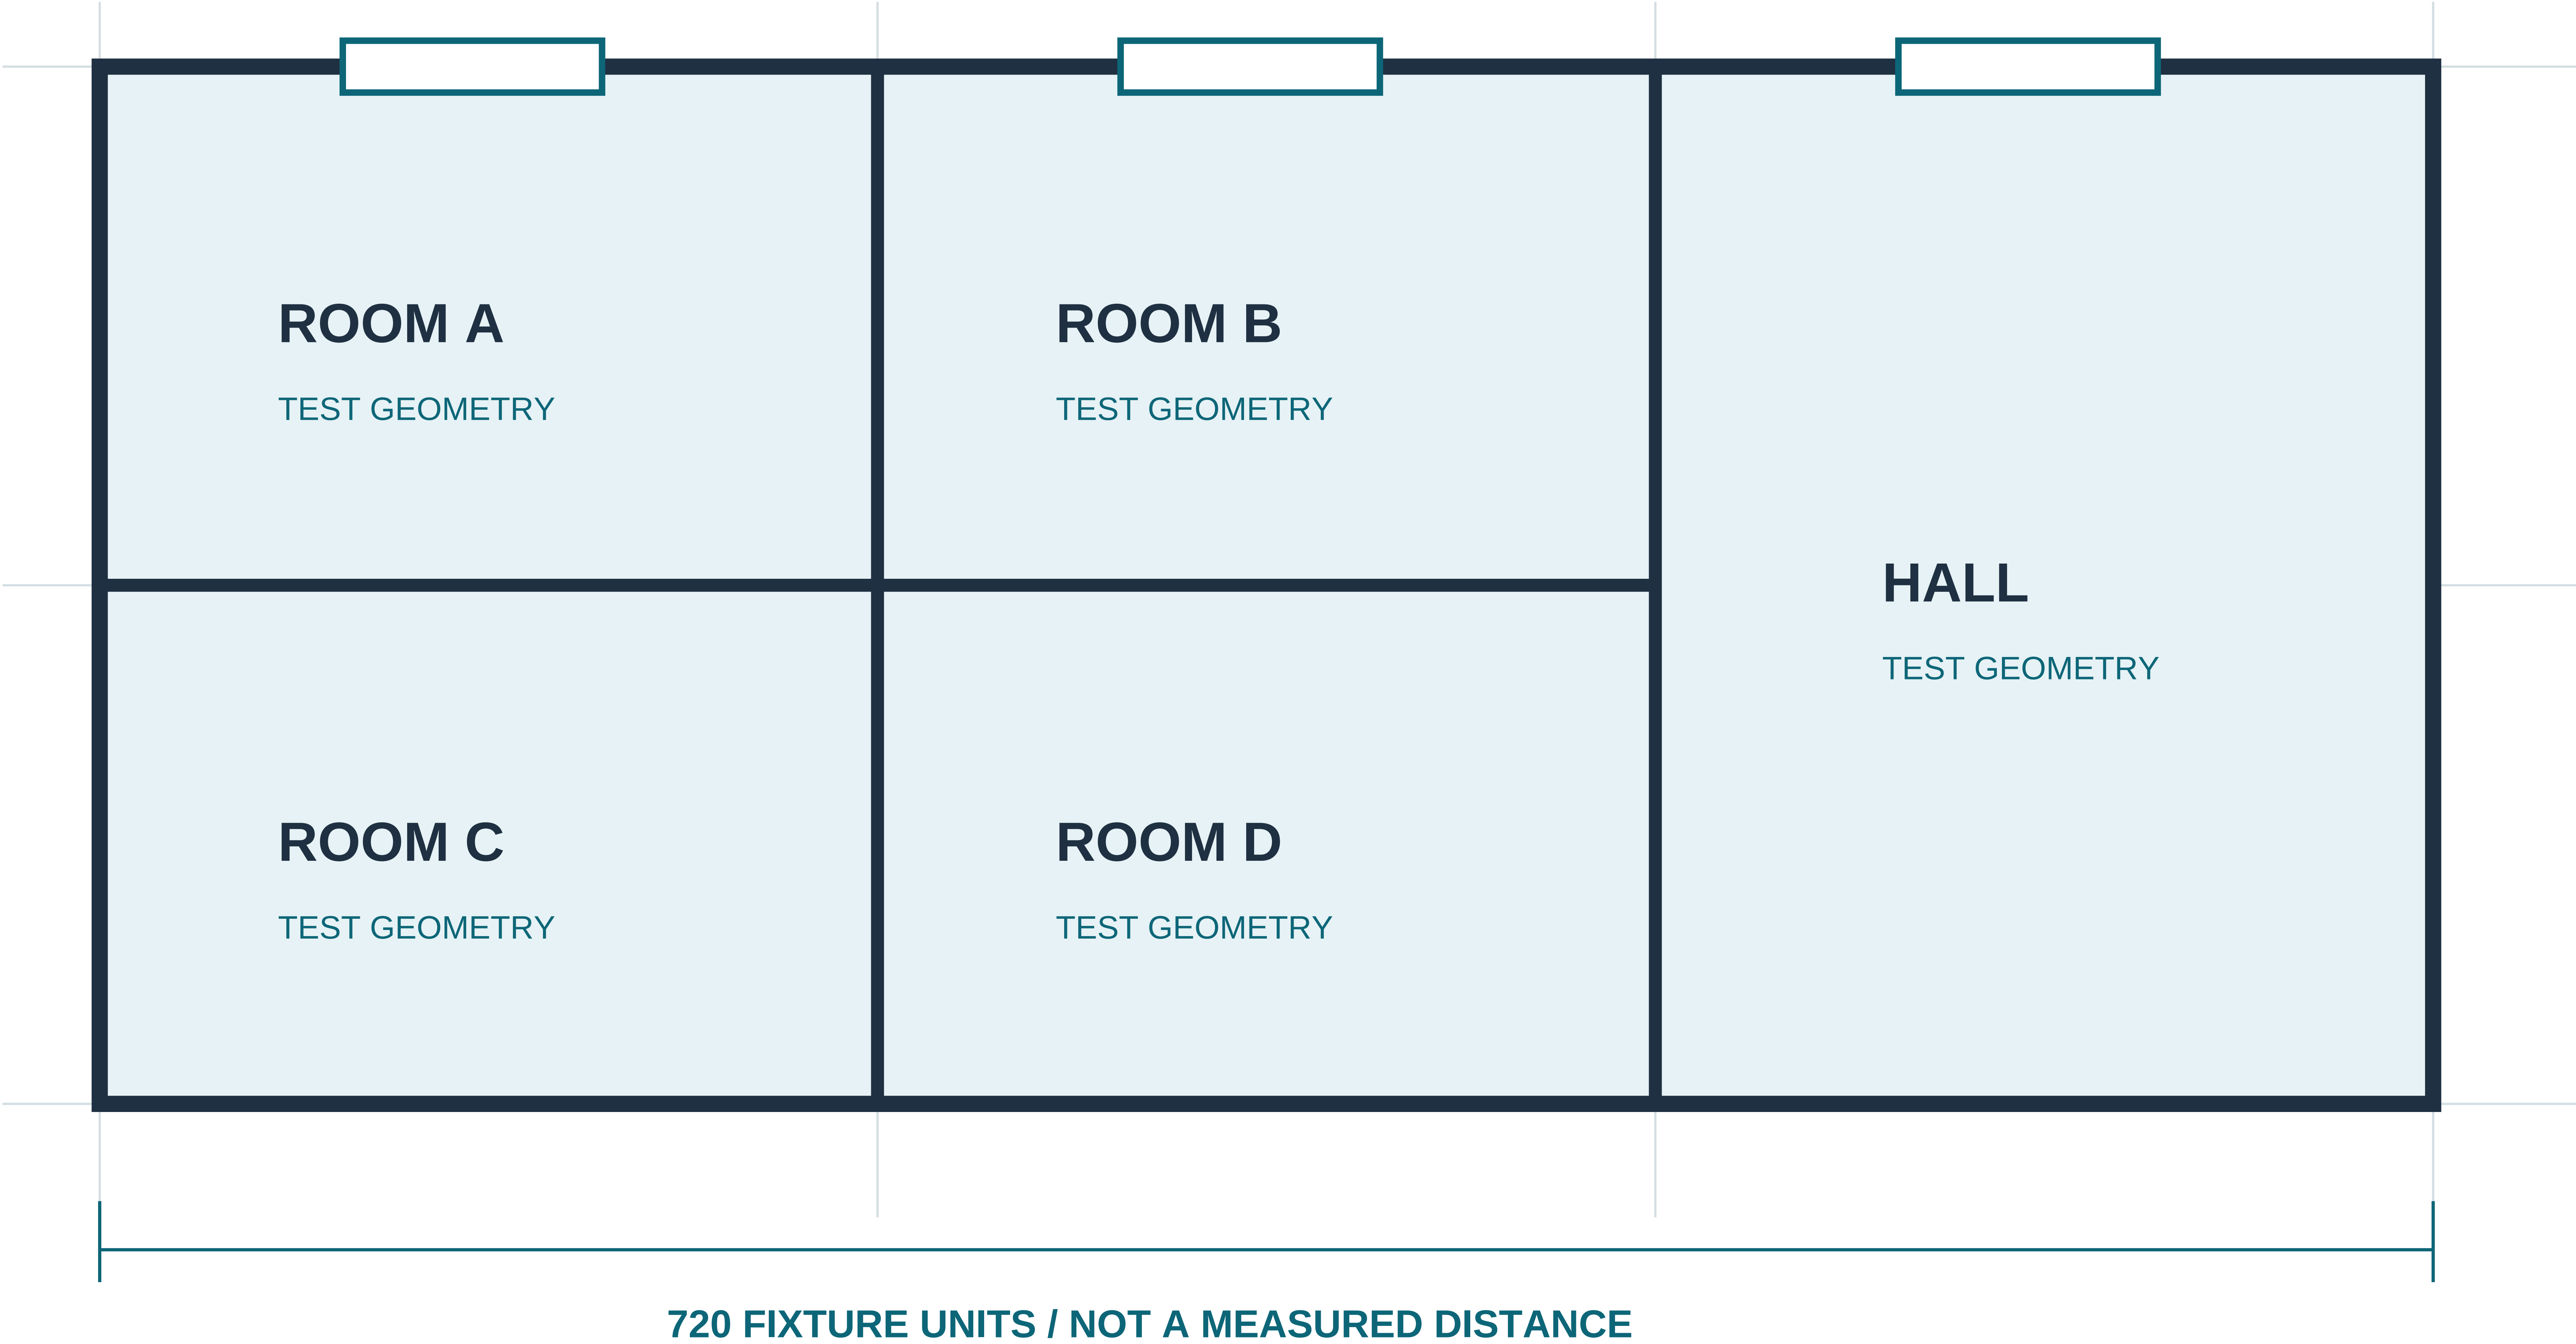

A-201 / SYNTHETIC SECTION

SYNTHETIC - NOT FOR CONSTRUCTION

No real site or design. Diagram coordinates are uncalibrated fixture units.

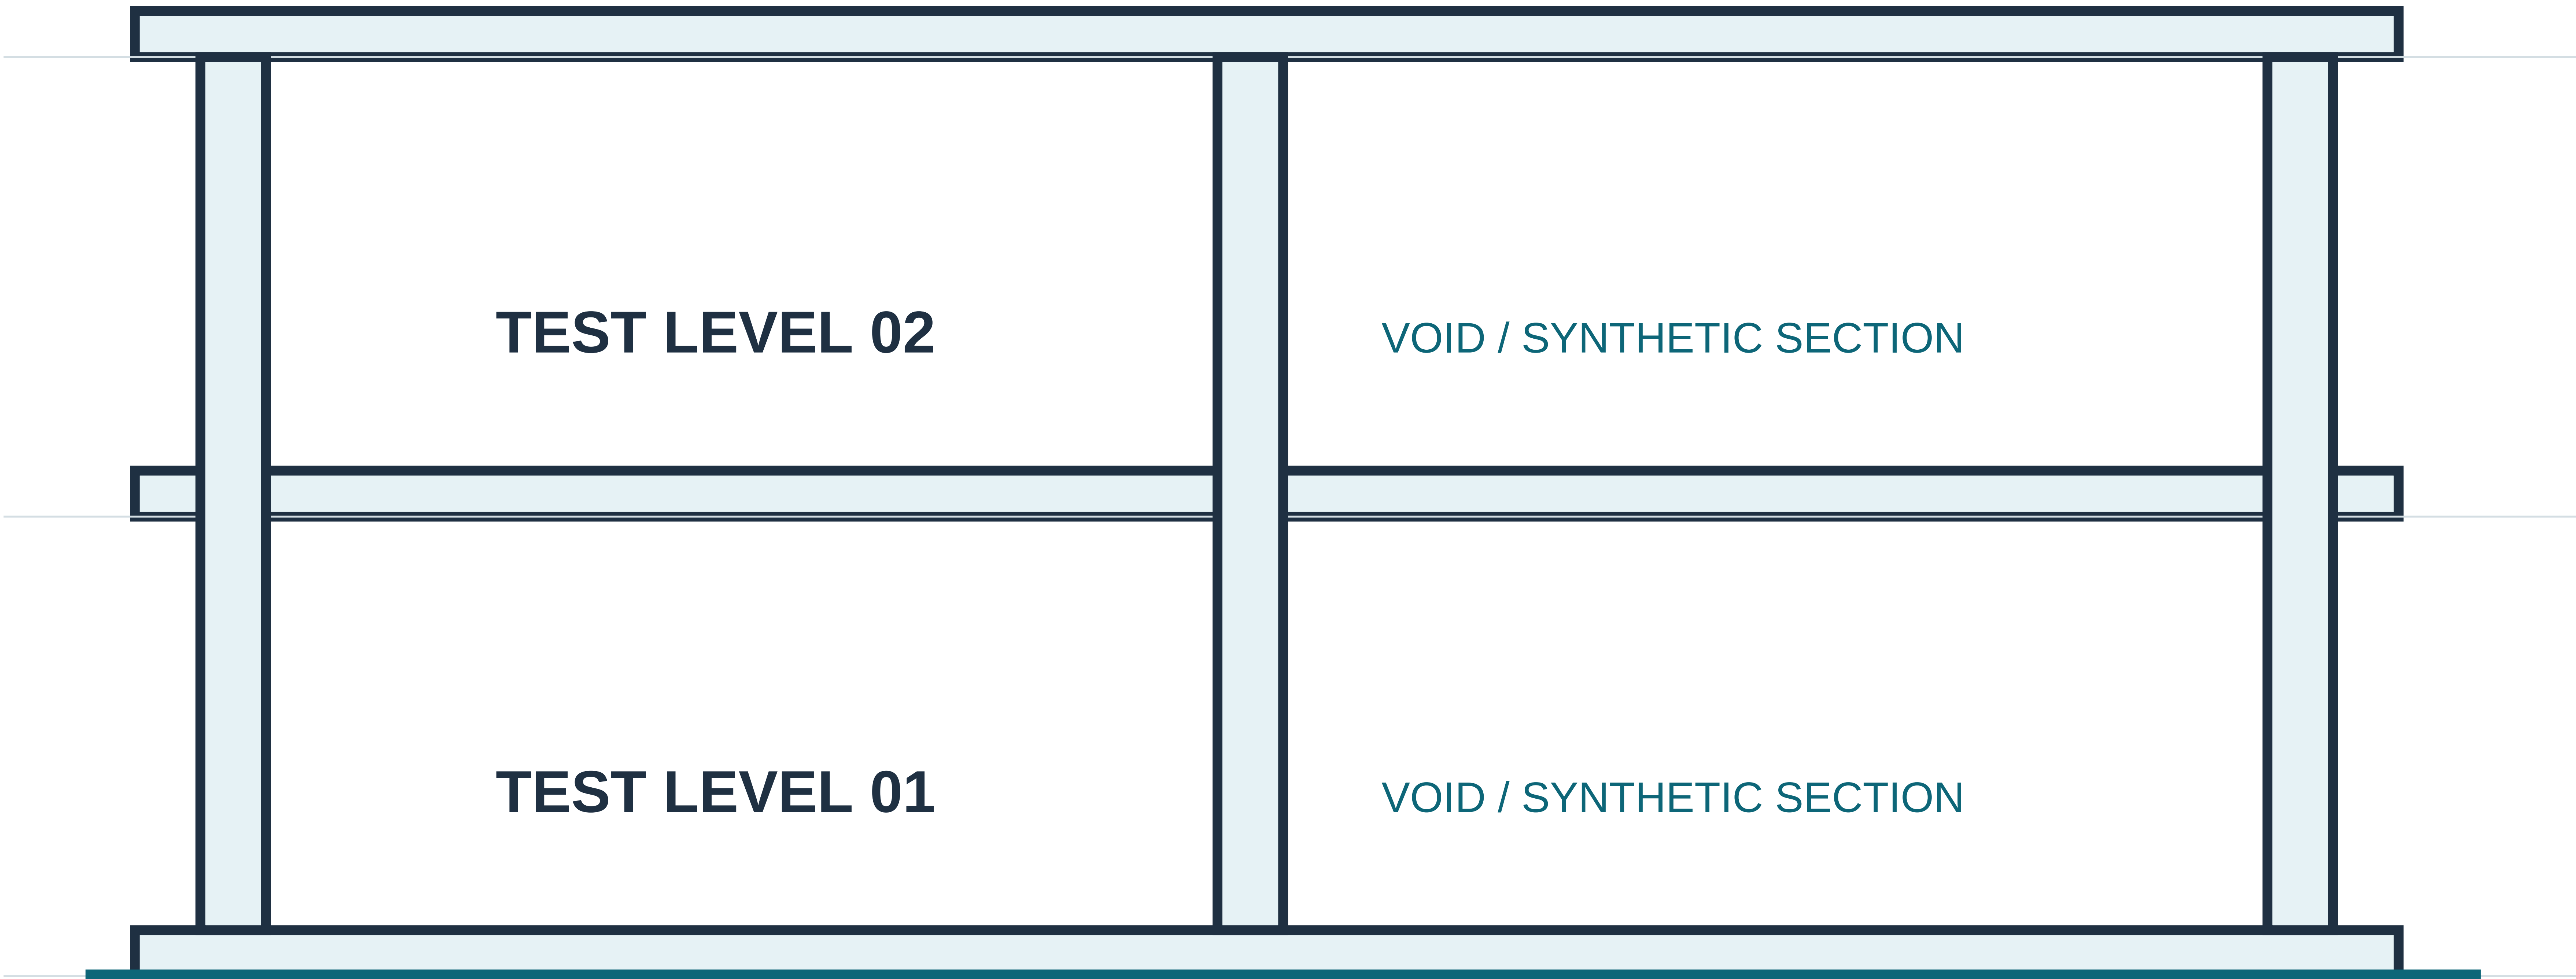


SECTION A-A / UNCALIBRATED

D-301 / SYNTHETIC DETAIL

SYNTHETIC - NOT FOR CONSTRUCTION

No real site or design. Diagram coordinates are uncalibrated fixture units.

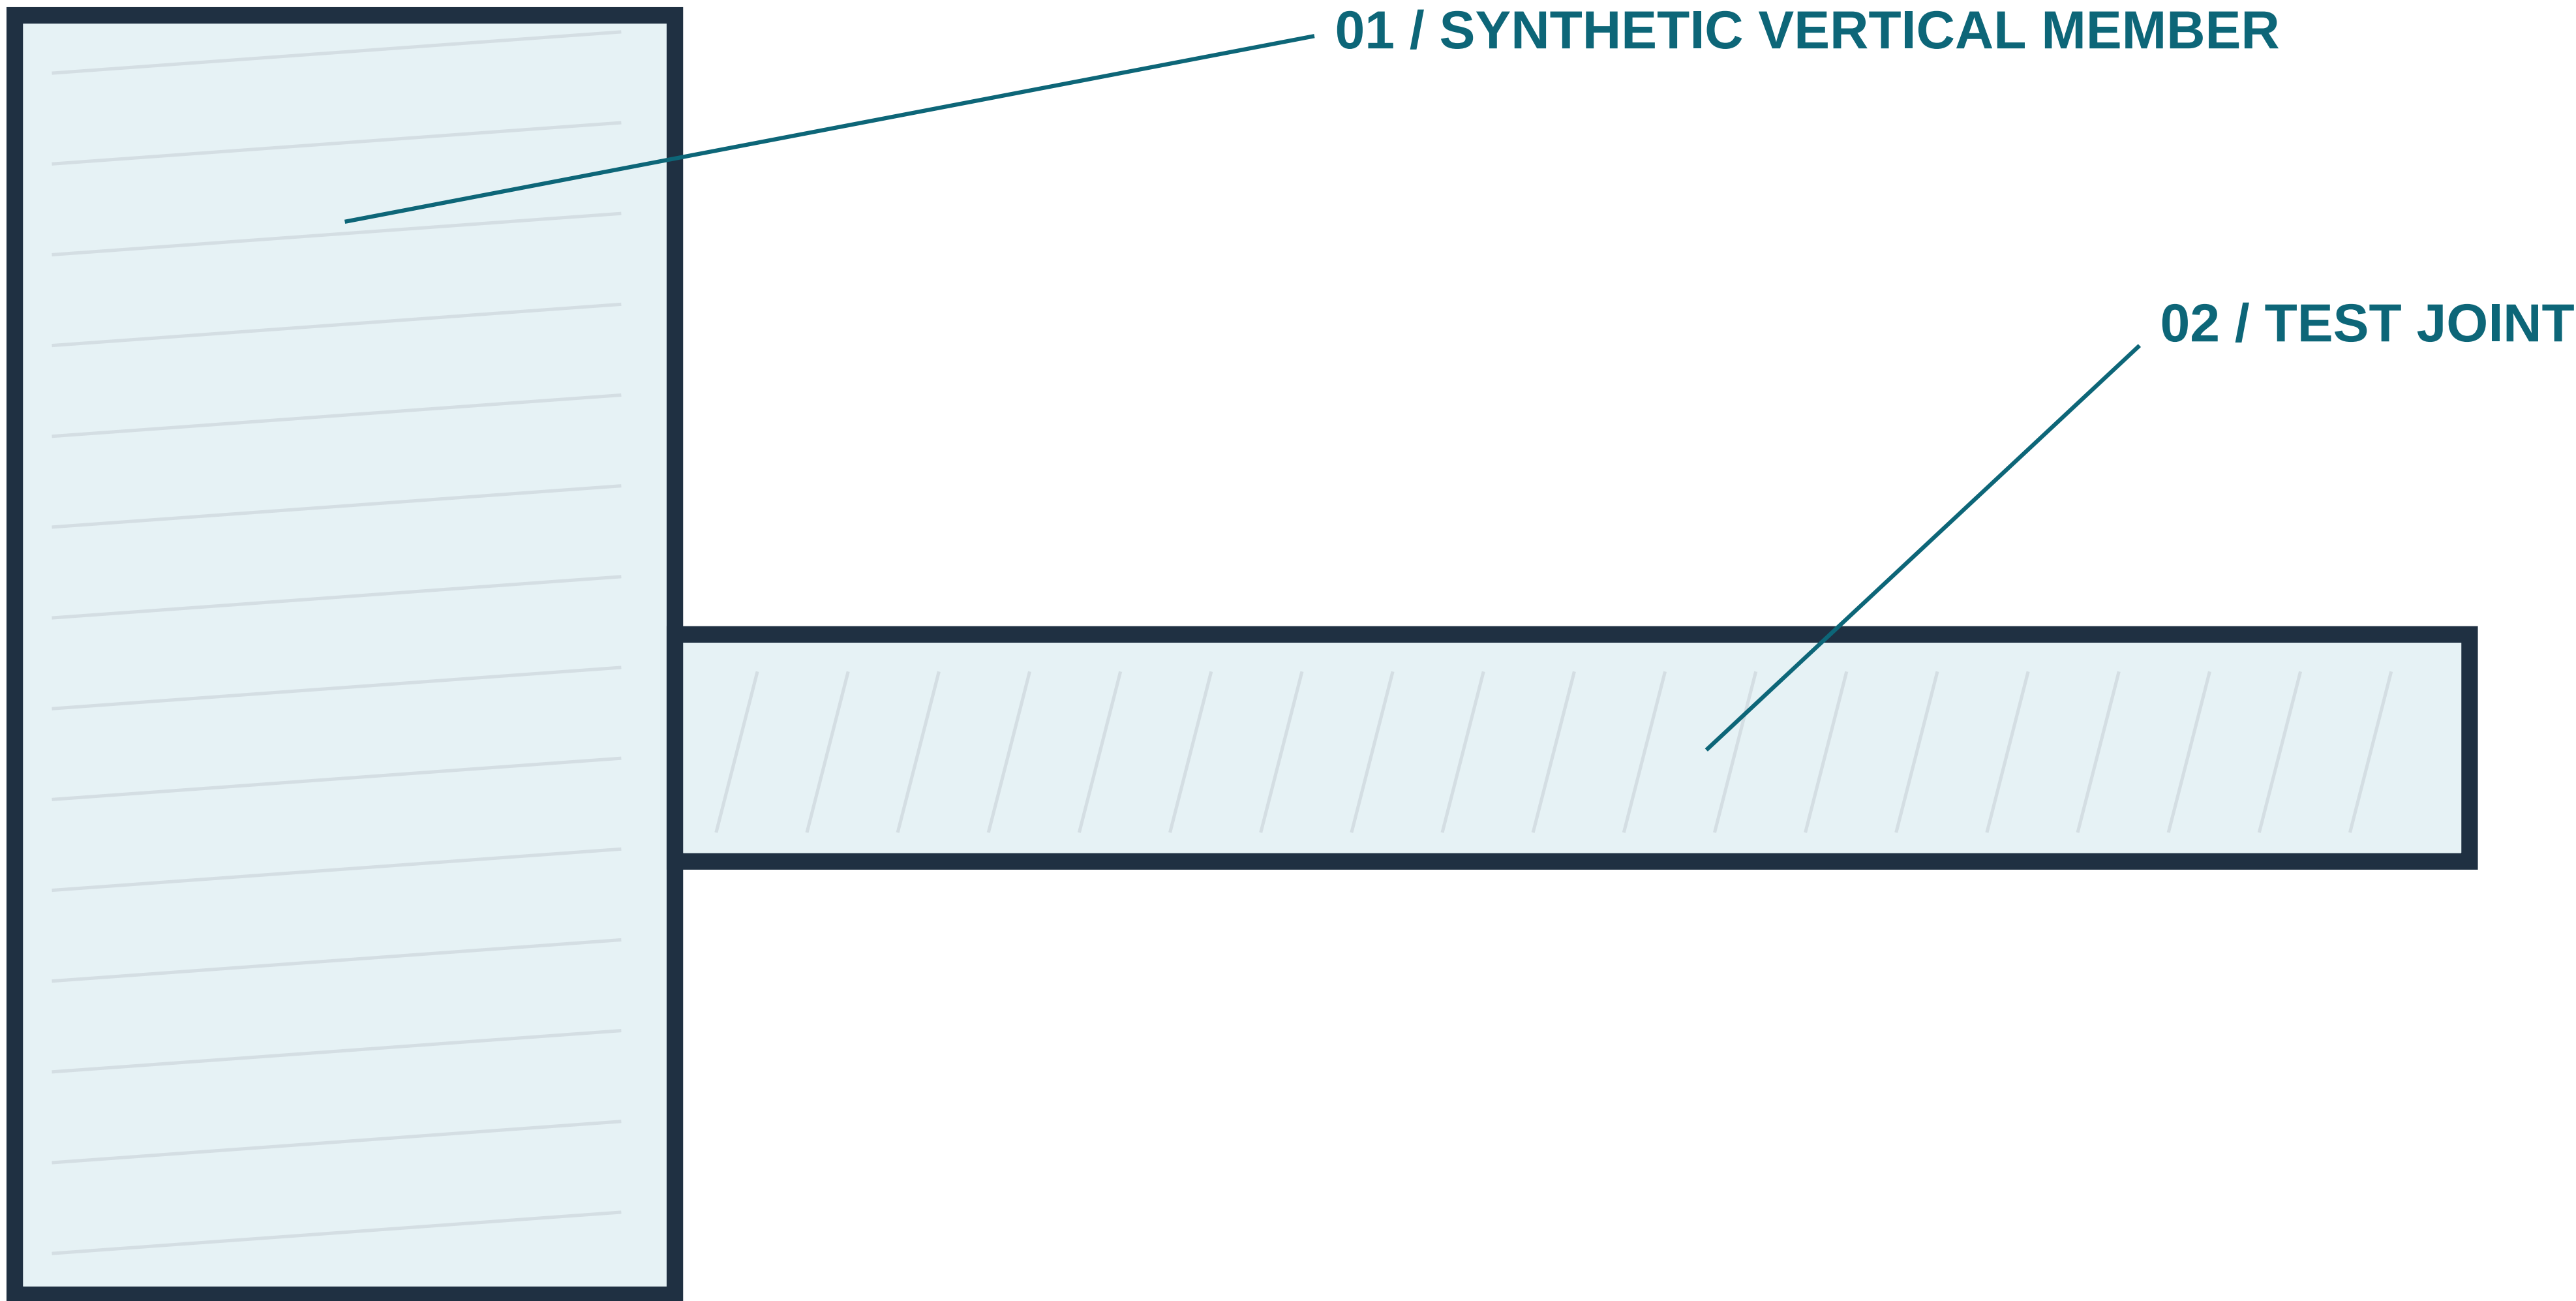

DETAIL 01 / VECTOR RENDERING SAMPLE